



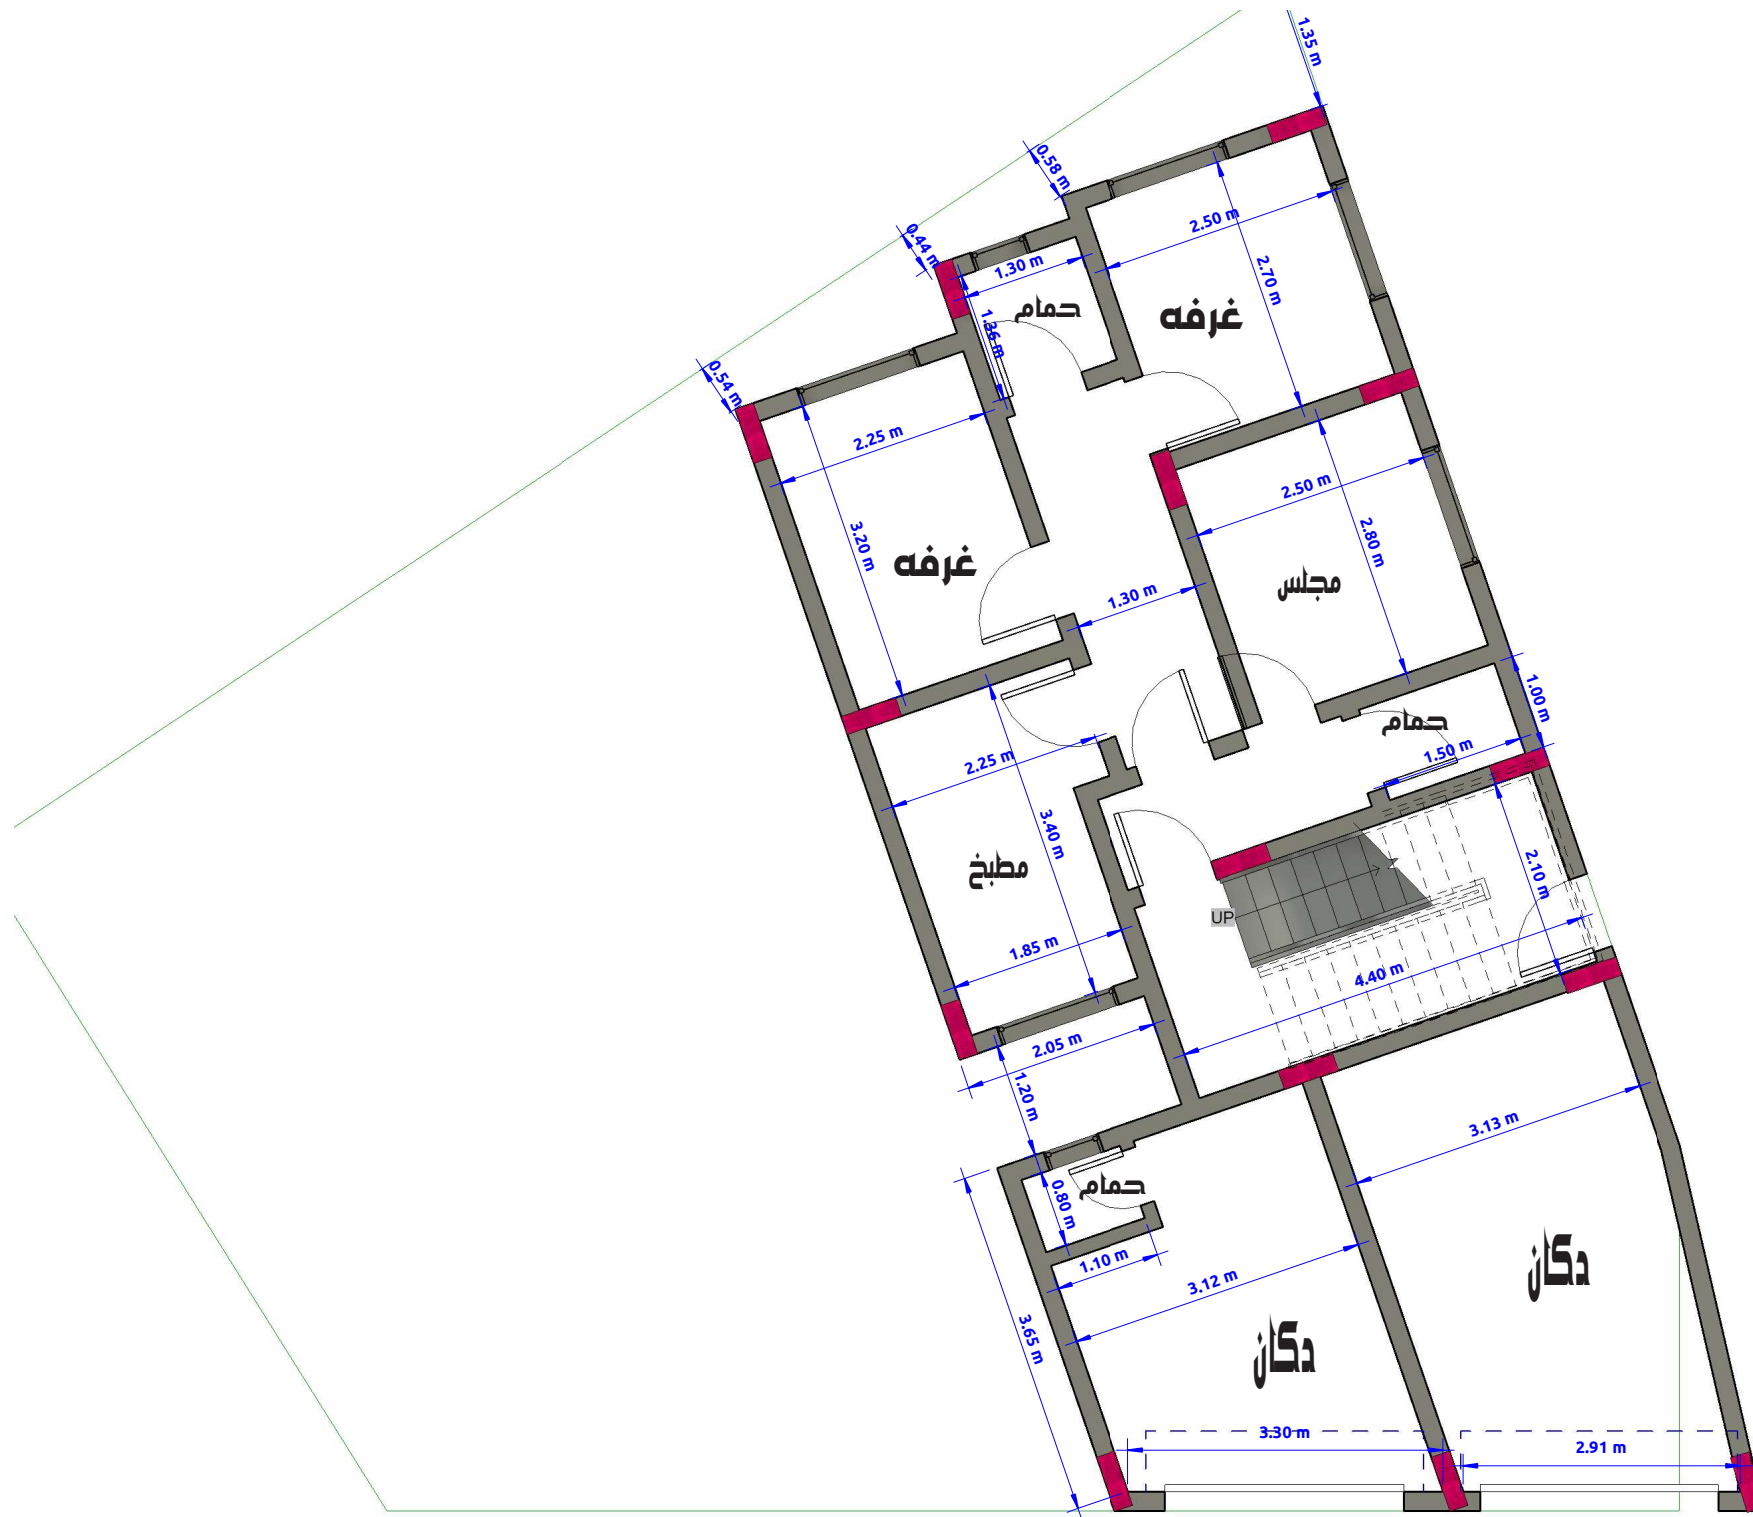

اسم المشروع: عمارة سكنية	نوع المخطط: معماري
موقع المشروع: متنه	اسم المخطط: مسقط الدور الارضي
المالك: صادق العكيشي	رقم الصفحة:
تصميم: م / اسامة سند	مقياس الرسم: 1 / 100
التاريخ: 2025/05/01	

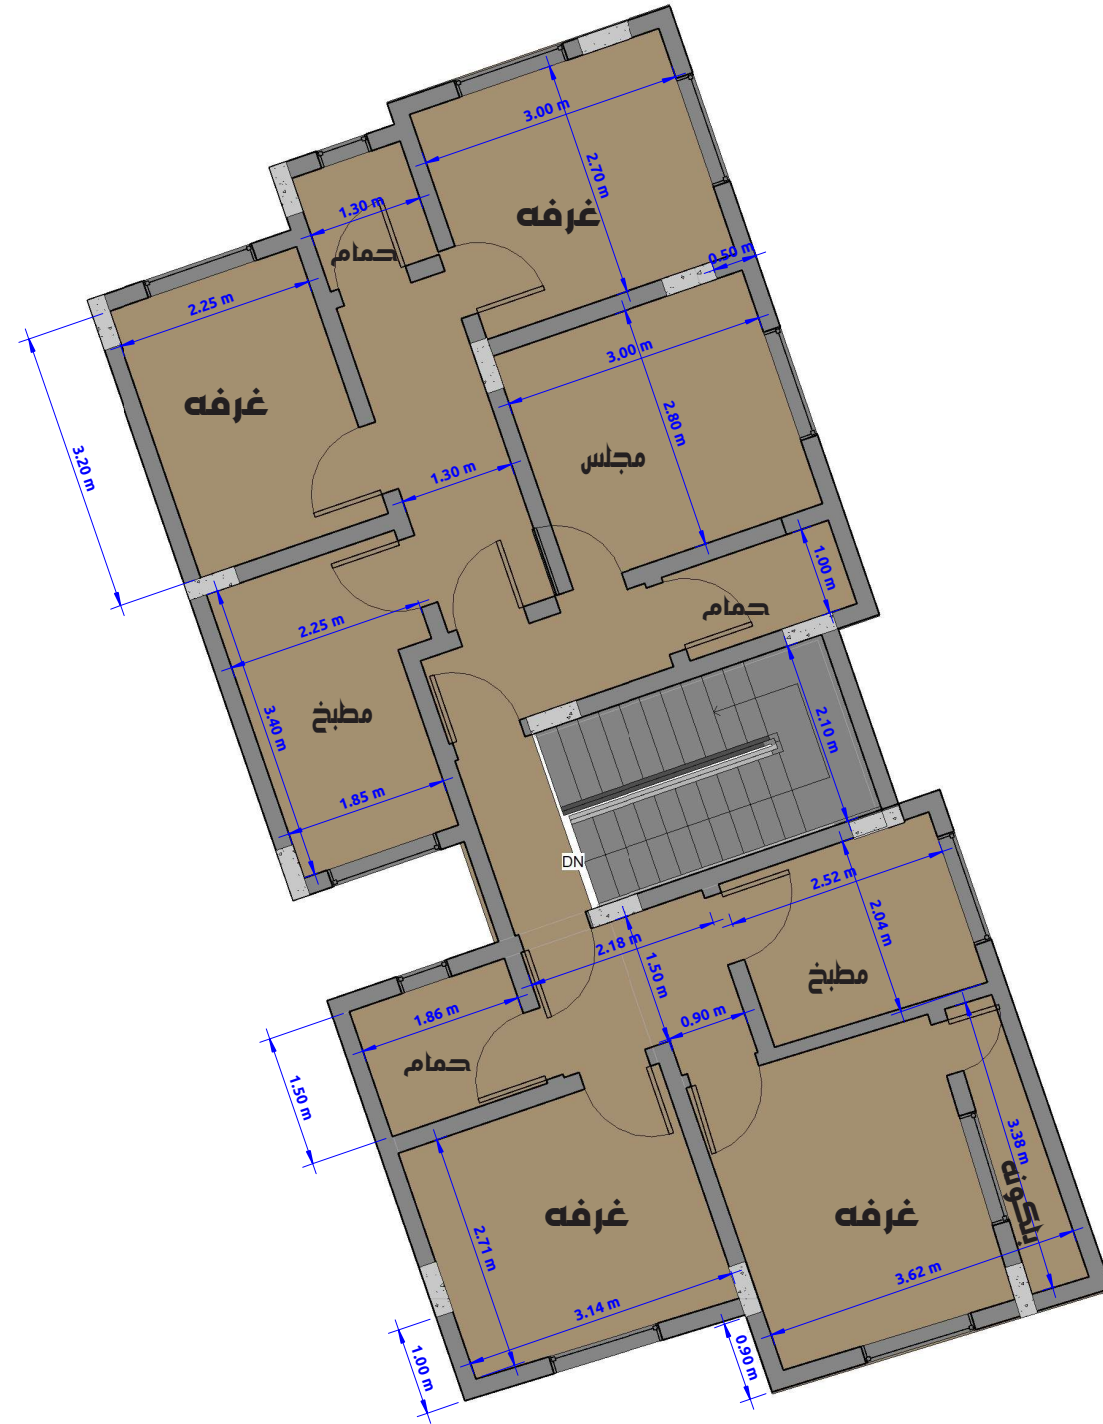

اسم المشروع: عمارة سكنية	نوع المخطط: معماري
موقع المشروع: متنه	اسم المخطط: مسقط الالدور المتكرر
المالك: صادق العكيشي	رقم الصفحة:
تصميم: م / اسامة سند	مقياس الرسم: 1 / 100
التاريخ: 2025/05/01	